


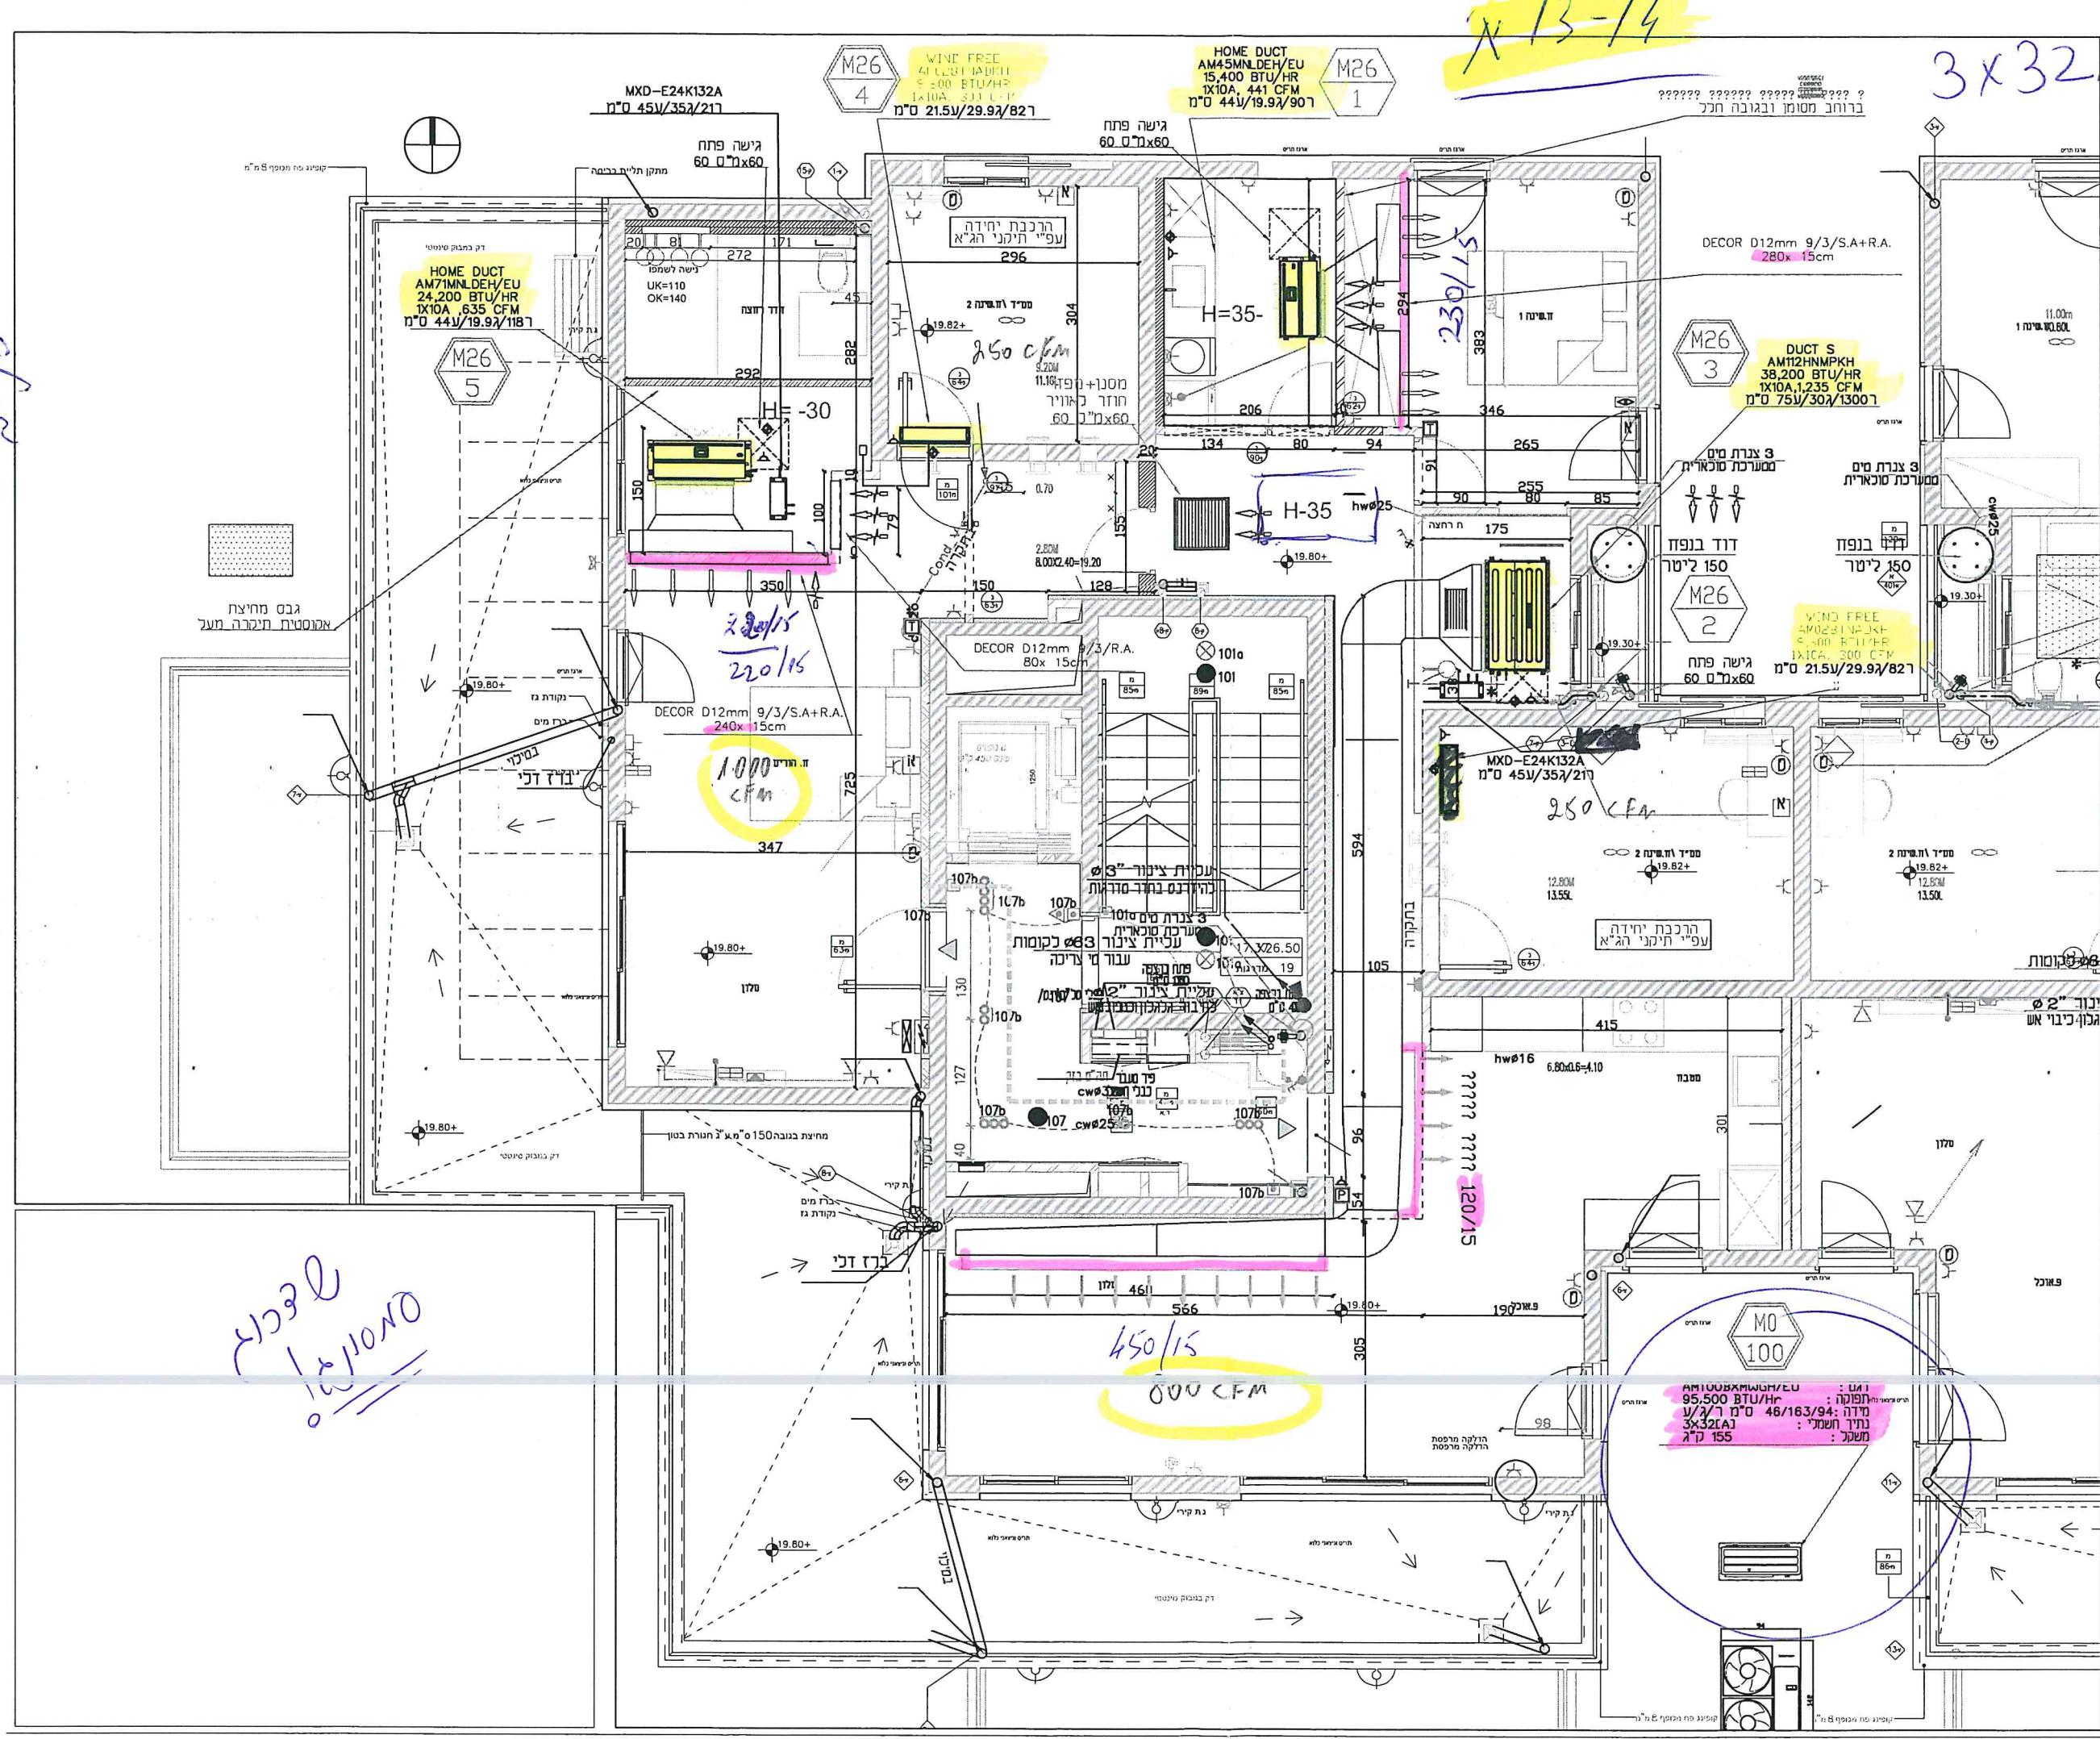

אין לראות בתוכנית אלו כתובות לביצוע
אלא רק לאחר אישור מהנדס מיזוג אוויר
ומפקח הפרויקט.

מקרא

נקודת ניקוז
נקודת הזנת חשמל - מסלול בחזרת הבטון
נקודת הזנת חשמל - 3
חומסס הפעלה חודד/מטבח
חומסס הפעלה
פנל שלמה מרכזי
ענייני

הערות

1. ניקוז בקוטר 32 מ"מ ליחידות פנימיות יש בבודד את צינור הניקוז למניעת עיבוי.
2. מידות תעלות הן נטו למעבר אוויר, בהתקנת תעלה אקוסטית יש להוסיף 5 ס"מ עבור בידוד בעובי 1".
3. על הקבלה לאשר מוכח חברת SAMS SYSTEMS את אורכי צנרת הנחושת בהתאם למידות בפועל לפני ביצוע.
4. על הקבלה לקבל את אישורו של קונסטרוקטור המבנה לאופן חיתוך היחידות הפנימיות וכן את אישורו לעמדת היחידות החיצוניות ומשקלן.
5. נידרש פתח גישה למזגן עבור כוח החשמל והניקוז.
6. במסמך יחידה החיצונית יש כדאוג לנקודת ניקוז תאורה ואזור בטוח לשירות ואחזקה ע"י סכנאי.
7. יש כדאוג למעבר אוויר חופשי ליחידה החיצונית. ולהימנע מקצרי אוויר.
8. התוכנית אינה כוללת היחידות כתי" 1001.
9. המשקלים המצויינים מתייחסים ליחידות סטנדרטיות וסיסטמאירי בלבד אלא אם מצויין אחרת.
10. על הקבלה לתעל אוויר חוזר ע"י תעלות פח מבודדות מפתחי יניקת אוויר חוזר אל פתחי הניקה ביחידות המיזוג הפנימיות וכל נדרש ע"י מכוני הנדסה הישראלי יש לעגור/לשמן את המעבה לבסיס הבטון או הגישטל כך שלא יפוך מרוח צד.
12. התוכנית/סכמת הצנרת המצורפת הינה כללית ודיאגרמת הדרושים להפעלה תקינה ומשלמת של המערכת.
13. יש לחבר תעלת אספקה עד למפוזר האוויר כדי כמנוע קצר אוויר בתוריות משוכבים.
14. ליחידה חתונה ניתן לשלב סימון שבועי.
15. יחידות העיליות/קסטות ניתנות להפעלה ע"י שלט אחיד.
16. במידה והגמיש המוגדר בתוכנית ארוך מ-4.5 מ"מ יש להוסיף מתאם פח להפרדת תרמית/אש.
17. באחריות הקבלה לוודא שאין מעג בין אלמנטים חשמליים למובילי אוויר.
18. אין לינוע אוויר חוזר מתוך חדרי שירותים

התוכנית הינה רכוש SAMS SYSTEMS. בבנין אין להשתמש בה או לא לצורך ביצוע הפרויקט המצויין במסמך. אין לשכפל כלשהו או להעתיק אותו או את הרעיונות האחרים בהן - בכל דרך שהיא - כללית בכתב מ SAMS SYSTEMS.

המבצע אחראי לבדיקת התוכנית. עליו לבדוק את כל הודעות התאמת-בטון ואת מצב המבנה וגובהו. על כל שעות או אי התאמה יש לדווח ל SAMS SYSTEMS.

שלב	כתיבה	כאשר	למכרז	לביצוע
0				
מחזור				

מס'	מחזור השינוי	תאריך	מאשר
3			
2			
1			
שינויים			
קמ:	1:50	תאריך: 8.12.2024	קובץ:
הוצגו:	דורון	שם: דורון	מס' דרי: 1
מס' פרויקט:	מס' דף: 1	מחזור: 1	
העבודה:	נזאי מרשל תא - דירה 26,25		
התוכנית:	מיזוג אוויר		
קבלה:	שרות הוגן		

SAMS SYSTEMS
AIR CONDITIONING
WWW.SAMS SYSTEMS.CO.IL
03-9335357 :טלפקס 03-9335433 :טל