מיזוגים

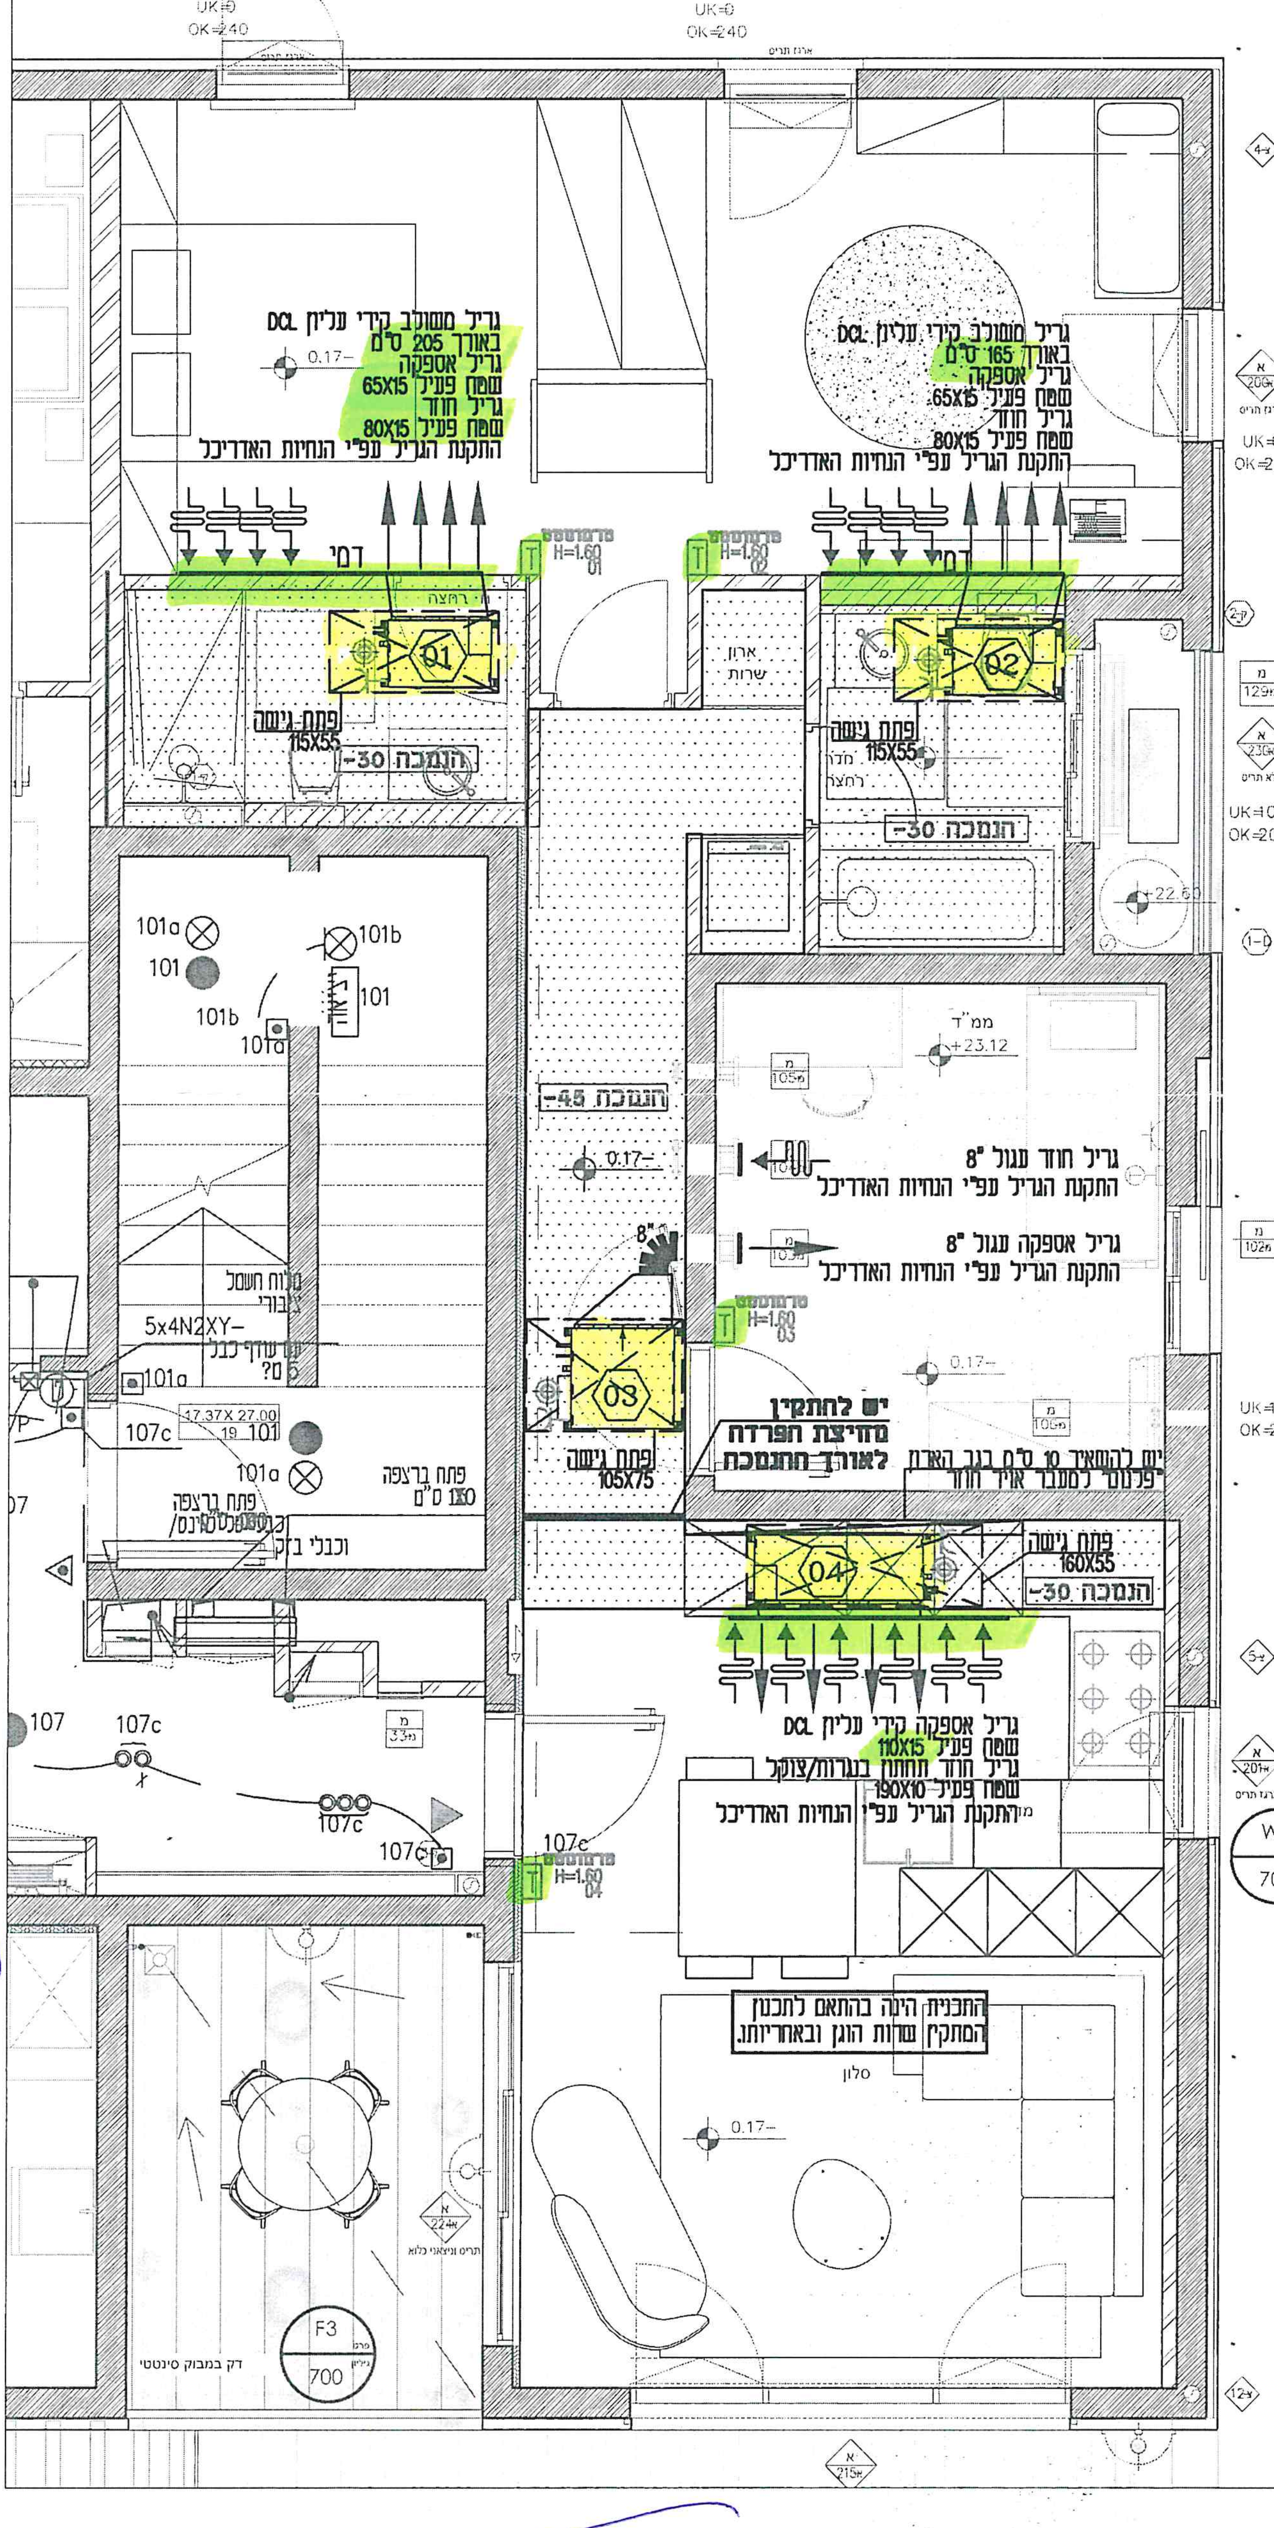

MITSUBISHI VRF

PUMY-SP140YKM
105/36/98(H)

מפסק פקט עם נעילה
גודל מאמ"ת:
3X16A

דגם:	01 PEFY-P40VMX
מידות	70/45/20
תפוקה	441 CFM
קירור:	15,400 BTU/hr
	2.12 A

דגם:	02 PEFY-P40VMX
מידות	70/45/20
תפוקה	441 CFM
קירור:	15,400 BTU/hr
	2.12 A

דגם:	03 PEFY-P32VMS
מידות	79/70/20
תפוקה	350 CFM
קירור:	12,300 BTU/hr
	0.75 A

דגם:	04 PEFY-P63VMX
מידות	115/45/20
תפוקה	689 CFM
קירור:	24,200 BTU/hr
	2.43 A

יח' מס' 4
תתקן אמני
טופס 4
באחריות דייר לבצע:
נק' חשמל, נק' ניקוז במטבח למי'
סגירות גבס. (דייר חתם ויודע).

פרויקט:	לואי מרשל 41
דירה:	קומה 7 דירה 16ב 32
תכנית	מיזוג אויר
קנ"מ 1:50	תאריך 20.11.24	מהדורה 01

שדרת מיזוגים.

32 נ' ע

9/6

מיזוגים

27/05/25